

ห้องน้ำใกล้ฉันทน์

Hiding In The Nearest – ห้องน้ำใกล้ฉั่ม ไม่ได้หมายถึงเพียง “ตำแหน่ง” บนแผนที่ แต่หมายถึงห้องน้ำสาธารณะที่เข้าถึงได้ง่าย อยู่ใกล้ตัว และปรากฏอยู่ในทุกพื้นที่ โดยไม่รบกวนภูมิทัศน์หรือประสบการณ์ของสถานที่นั้น

และคุณค่าที่เพิ่มขึ้นของห้องน้ำสาธารณะก็ให้ความสุขแก่ผู้ใช้งาน




กลิ่น

ความเป็นส่วนตัวน้อย

Handwritten text in the circular inset:

- Top left: ๖๖ ๖๖ ๖๖
- Top center: ๖๖ ๖๖ ๖๖
- Top right: ๖๖ ๖๖ ๖๖
- Bottom left: ๖๖ ๖๖ ๖๖


เปรียบเทียบด้วยวิธีการวัดทางเหนือกันแต่ต่างรูปทรงเพื่อดูว่ารูปทรงใดเหมาะสมกับการพรางและไปตั้งอยู่ที่ใดก็ได้ จึงเลือกรูปทรงสามเหลี่ยมเพราะว่ารูปทรงสามเหลี่ยมช่วยลดการรับรู้มวลรวมของวัตถุ เนื่องจากไม่มีความหนาที่ชัดเจนให้สายตาจับเป็นรูปทรงหลัก เมื่อใช้ร่วมกับบนยอดเดียวจะทำให้ให้อ่อนเขตของวัตถุเลือนหายและดูอ่อนๆ เป็นส่วนหนึ่งของบริบทมากกว่าวัตถุเดียว

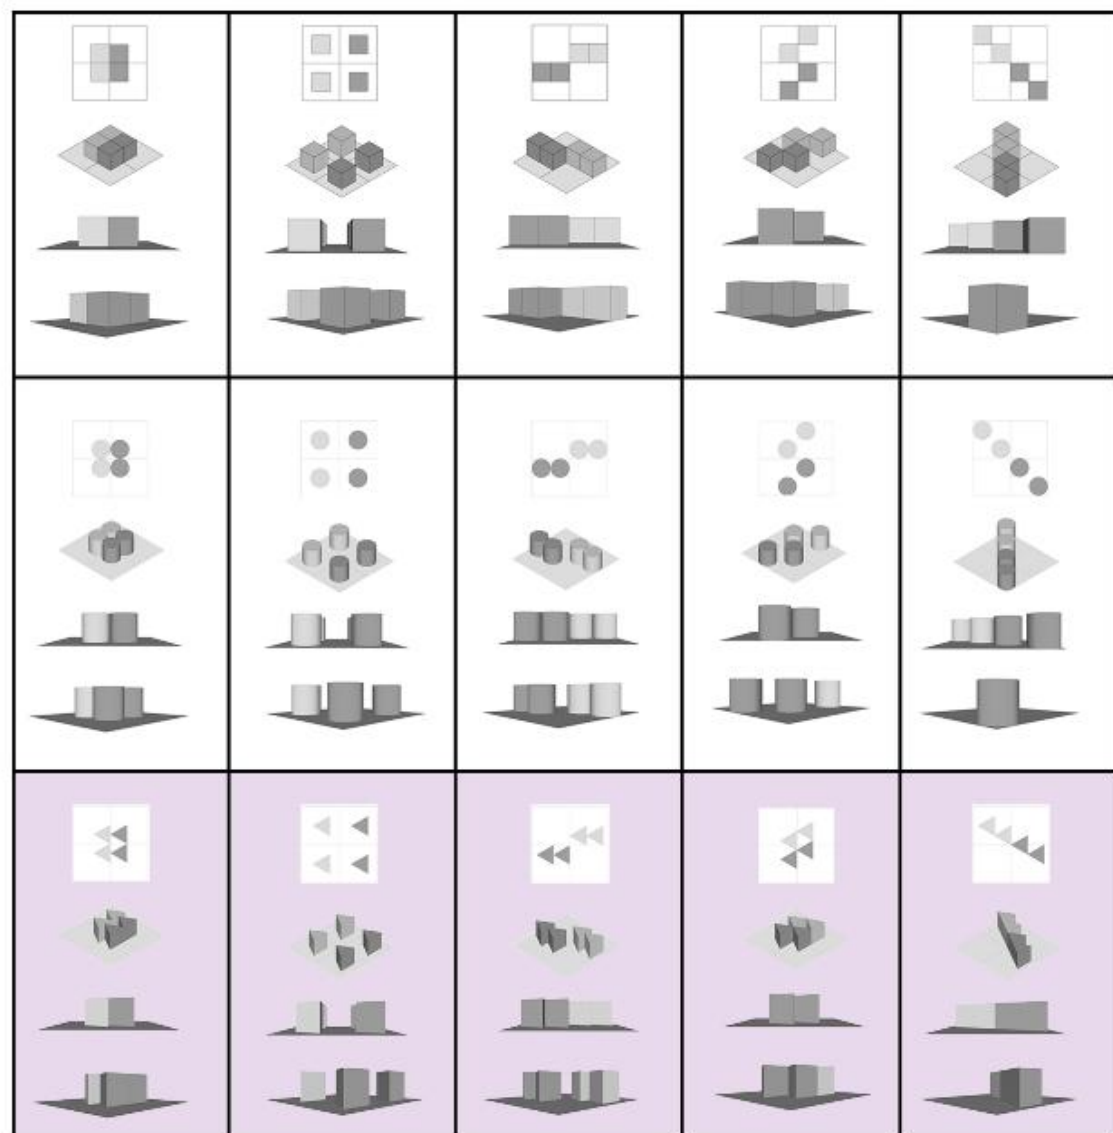

A horizontal strip of six black and white photographs showing various urban and natural scenes in Seoul. The images are: 1. A view of a river and a city skyline across the water. 2. A narrow alleyway with laundry hanging on lines and a person walking. 3. A paved path lined with trees and a fence. 4. A street scene with a traffic light and a person walking. 5. A group of people walking on a sidewalk, some holding umbrellas. 6. A view of a mountain range in the distance. Each photograph has a pink translucent paper flag overlaid on it, featuring a white silhouette of a person.

ที่ยกระดับขึ้นมาของห้องน้ำสาธารณะ: ในอีกแบบหนึ่ง เราเลือกนำเสนอเพียง 2 พื้นที่ทำน้ำ (โครงสร้างหลัก (MAIN STRUCTURE IDEA) และรอง (SHELL SYSTEM ALTHERNATIVE OPTION)) เพื่อให้เห็นถึงสภาพแวดล้อมที่ต่างกันสุดขั้ว ที่ห้องน้ำในแนวคิดนี้สามารถพรางและผสานตัวเองเข้ากับมันได้อย่างแนบเนียน

เป็นห้องนำสารธารณะที่พัฒนาโดยใช้โครงสร้างเดียวกันเป็นฐานการออกแบบ และสามารถปรับเปลี่ยนภาพลักษณ์ภายนอกผ่านวัสดุปิดผิวที่แตกต่างกันให้เข้ากับการใช้งานในบริบทที่หลากหลาย โดยอิงสัดส่วนความสูงจากระดับความเป็นส่วนตัวและช่องทางการระบายอากาศที่เหมาะสม

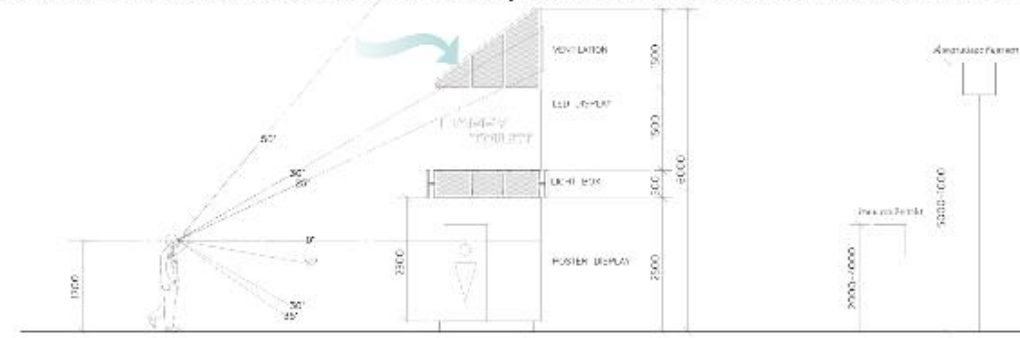

พนักงานส่วนบบ
สามารถปรับเปลี่ยนความสูงตา
ความต้องการได้ในแต่ละพื้นที่แ
มีช่องสำหรับการระบายอากาศ

โครงสร้างผนัง
โครงคร่าวเหล็ก 5x10 CM.
เชื่อมด้วย JOINT เหล็ก
STEEL PROFILE

— บานประตูเลื่อน
ติดผนัง-ขยับเข้า-ออก

พื
พืคองกริตสำเร็จรูป

1 ROOF FINISHING
TEMPERED GLASS

TRANSLUSENT FINISHING
POLYCARBONATE

MIRROR GLASS

PATTERN
CLASS

3 EXTERIOR SURFACE

ALUMINUM

MIRROR FINISH
STAINLESS STEEL

INSULATION

แผ่นฉนวนกับความร้อนและเสียง

STEEL PROFILE

TYPE 1

TYPE 2

TYPE 3

TYPE A




SIAM CENTER


LOCATION EXAMPLE (CITY CRASH)

เราเลือกที่จะนำเสนอตัวอย่างของห้องน้ำสาธารณะที่ปะทะและในขณะเดียวกันก็พรางตัวเข้ากับบริบทของเมืองที่มี ความหนาแน่นและความเคลื่อนไหวสูง เพื่อเป็นต้นแบบห้องน้ำที่สามารถอยู่ร่วมกับบริบทตามเส้นทางสาธารณะที่ แสดงถึงการเข้าถึงได้โดยง่ายโดยไม่ต้องวิ่งเข้าไปใช้งานภายในอาคารใดๆ


ปรับเปลี่ยนตัวเองตามด้วยระบบเปลี่ยนที่มีความเหมาะสมกับ สภาพแวดล้อมใดๆ ก็ตามที่ตัวห้องน้ำตั้งอยู่ ด้วยรูปทรง ขนาด ความสูงที่สร้างความเป็นส่วนตัว ไม่รบกวนสภาพแวดล้อมผู้ใช้งานสามารถทำธุระได้ อย่างไม่ต้องเกรงเหนียม จากปัญหาที่ยก ตัวอย่างในข้างต้นอีกต่อไป

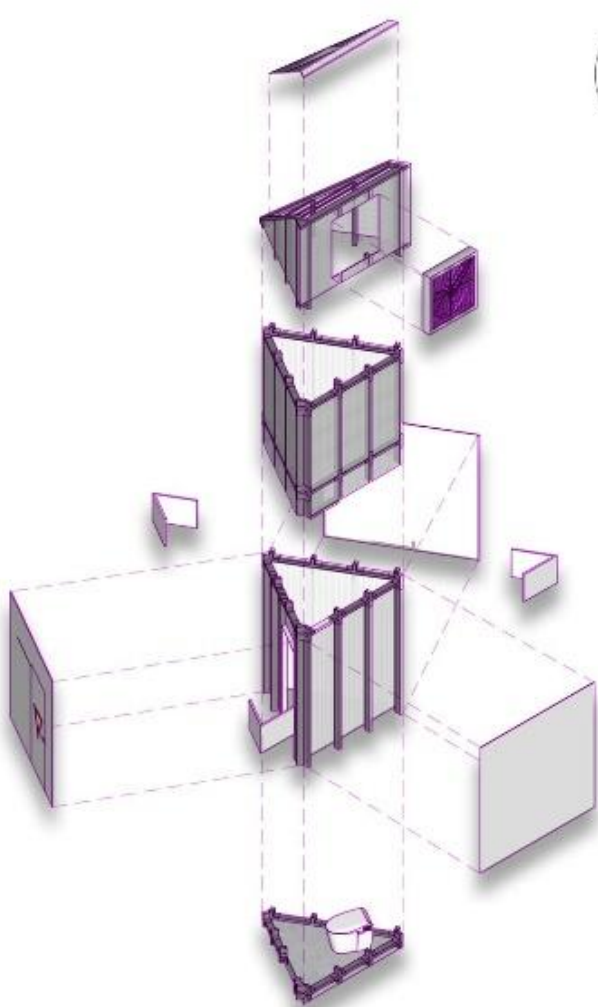


AXONOMETRIC

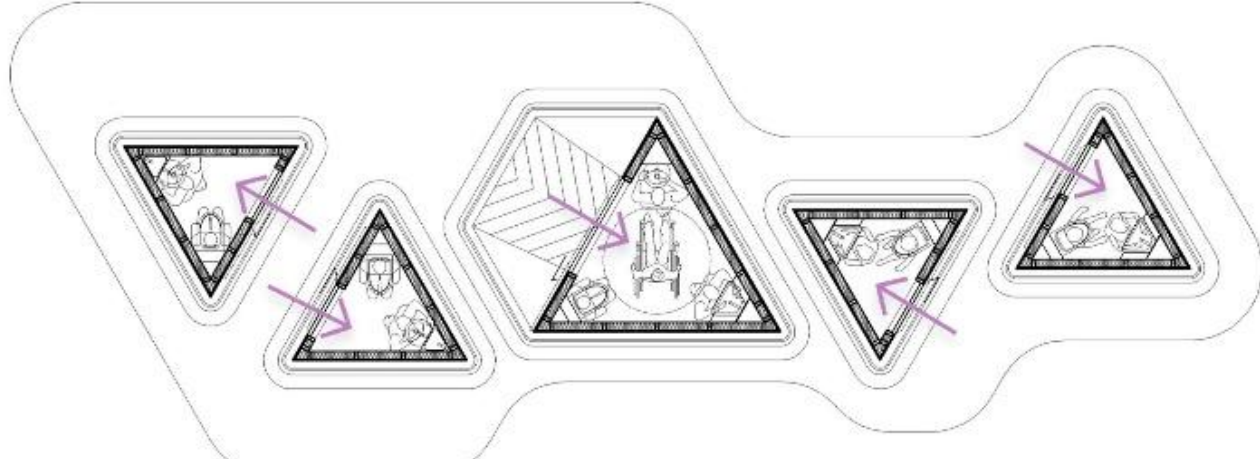


PLAN เรียงตัวทางยาวขนานไปกับแนวทางเดินเท้า มีห้องน้ำคพการอยู่ตำแหน่งกลางแยกชายหญิงออกไป
คนละด้านบดพอร์มเป็นทิศทางที่แตกต่างกัน สามารถประยุกต์ใช้กับพื้นที่ทางเดินเท้าที่ขยับขนาดรองรับ
เพียงพอในพื้นที่เมืองกรุงเทพมหานคร

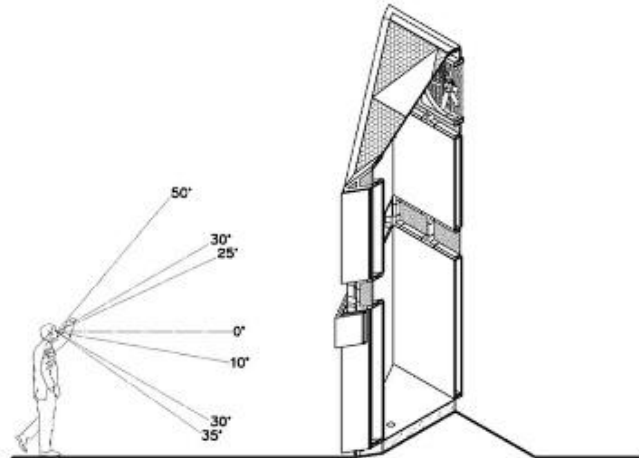

SCETION

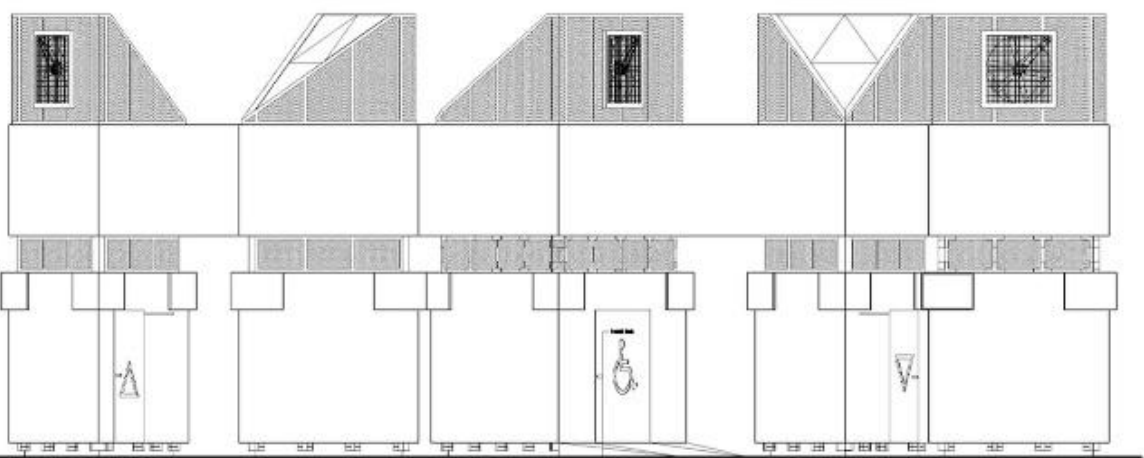

ELEVATION

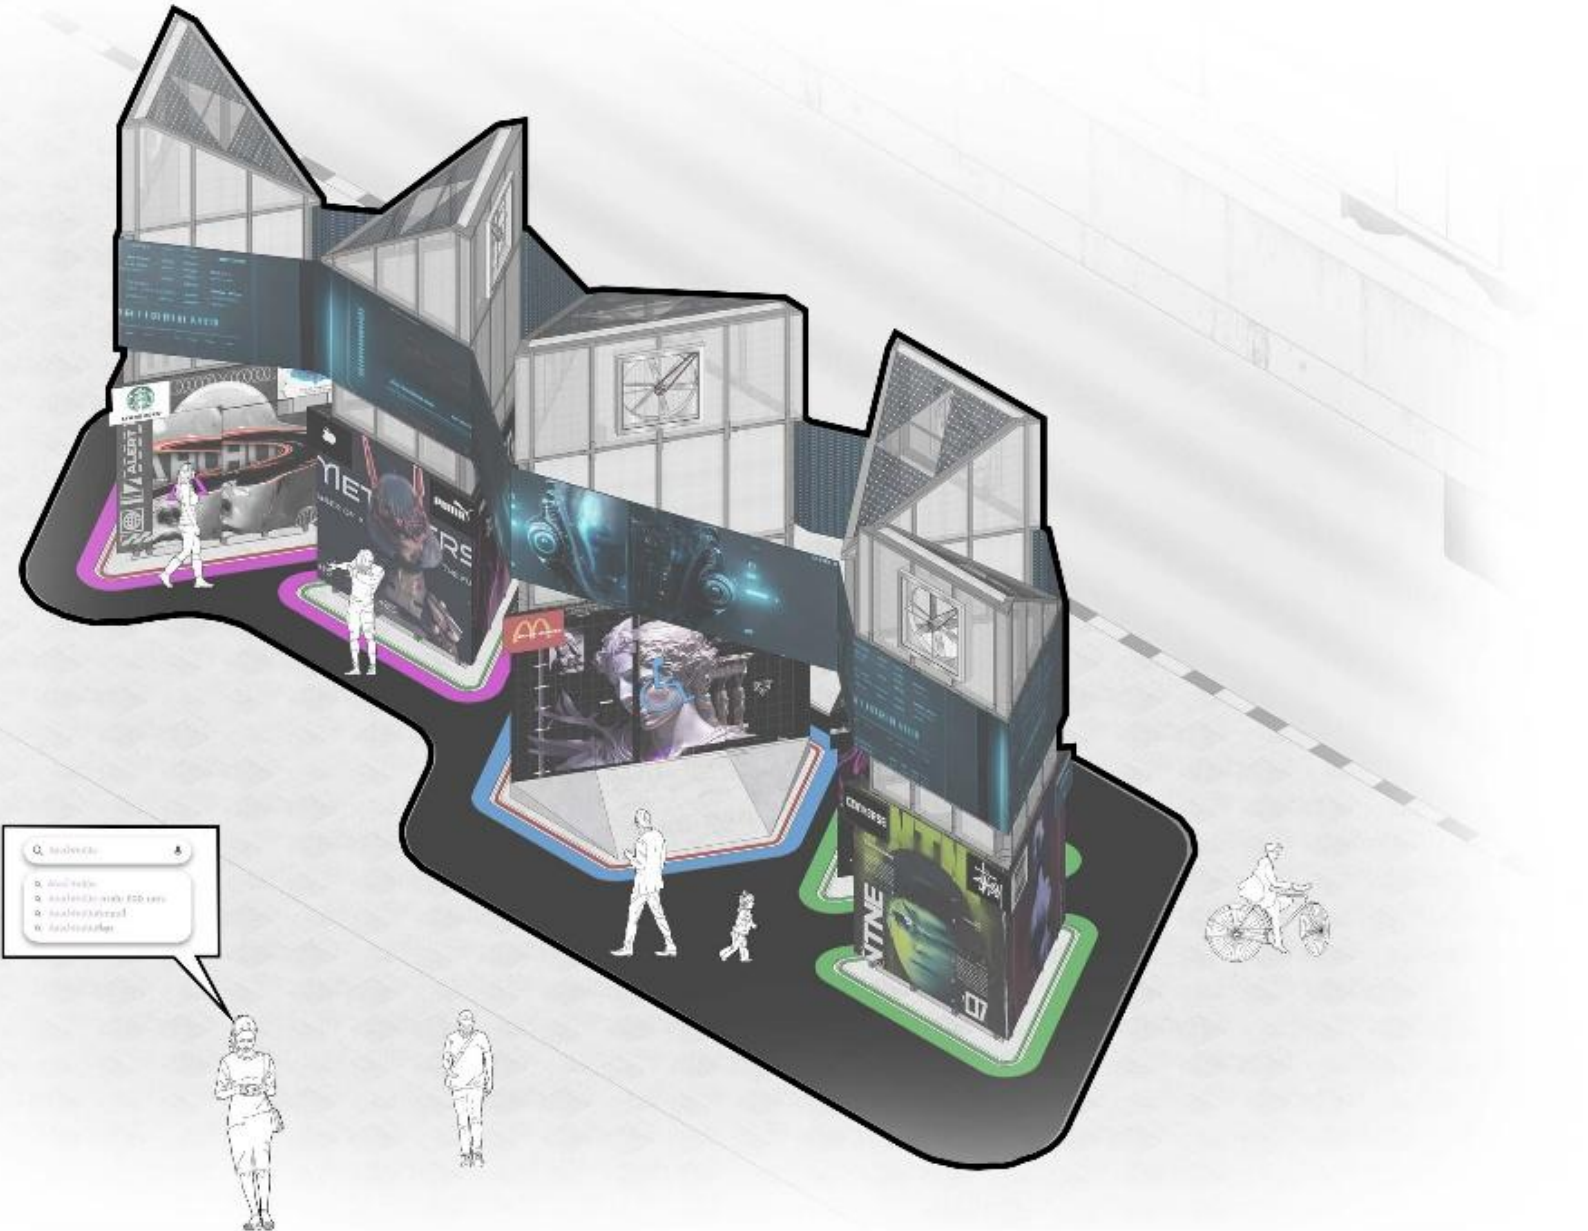





GREEN AREA

LOCATION EXAMPLE (NATURAL CLASH)

สำหรับการวางผังน้ำสาธารณะในพื้นที่สีเขียว ไม่ว่าจะเป็นสวนสาธารณะ อุทยานแห่งชาติ เราแสดงให้เห็นถึงระบบเปลือกที่สารละลายก่อน
เอาสภาพแวดล้อมโดยรอบมาเป็นส่วนหนึ่งของเปลือกอาคาร ทำให้เกิดความไม่ชัดเจนของรูปทรง เพื่อลดการรบกวนทางสายตาของผู้พบเห็นและผสานตัวห้องน้ำเข้าเป็นส่วนหนึ่งของสภาพแวดล้อมอย่างแนบเนียนเพื่อไม่ลดทอนคุณค่าความงามของธรรมชาติรอบตัว

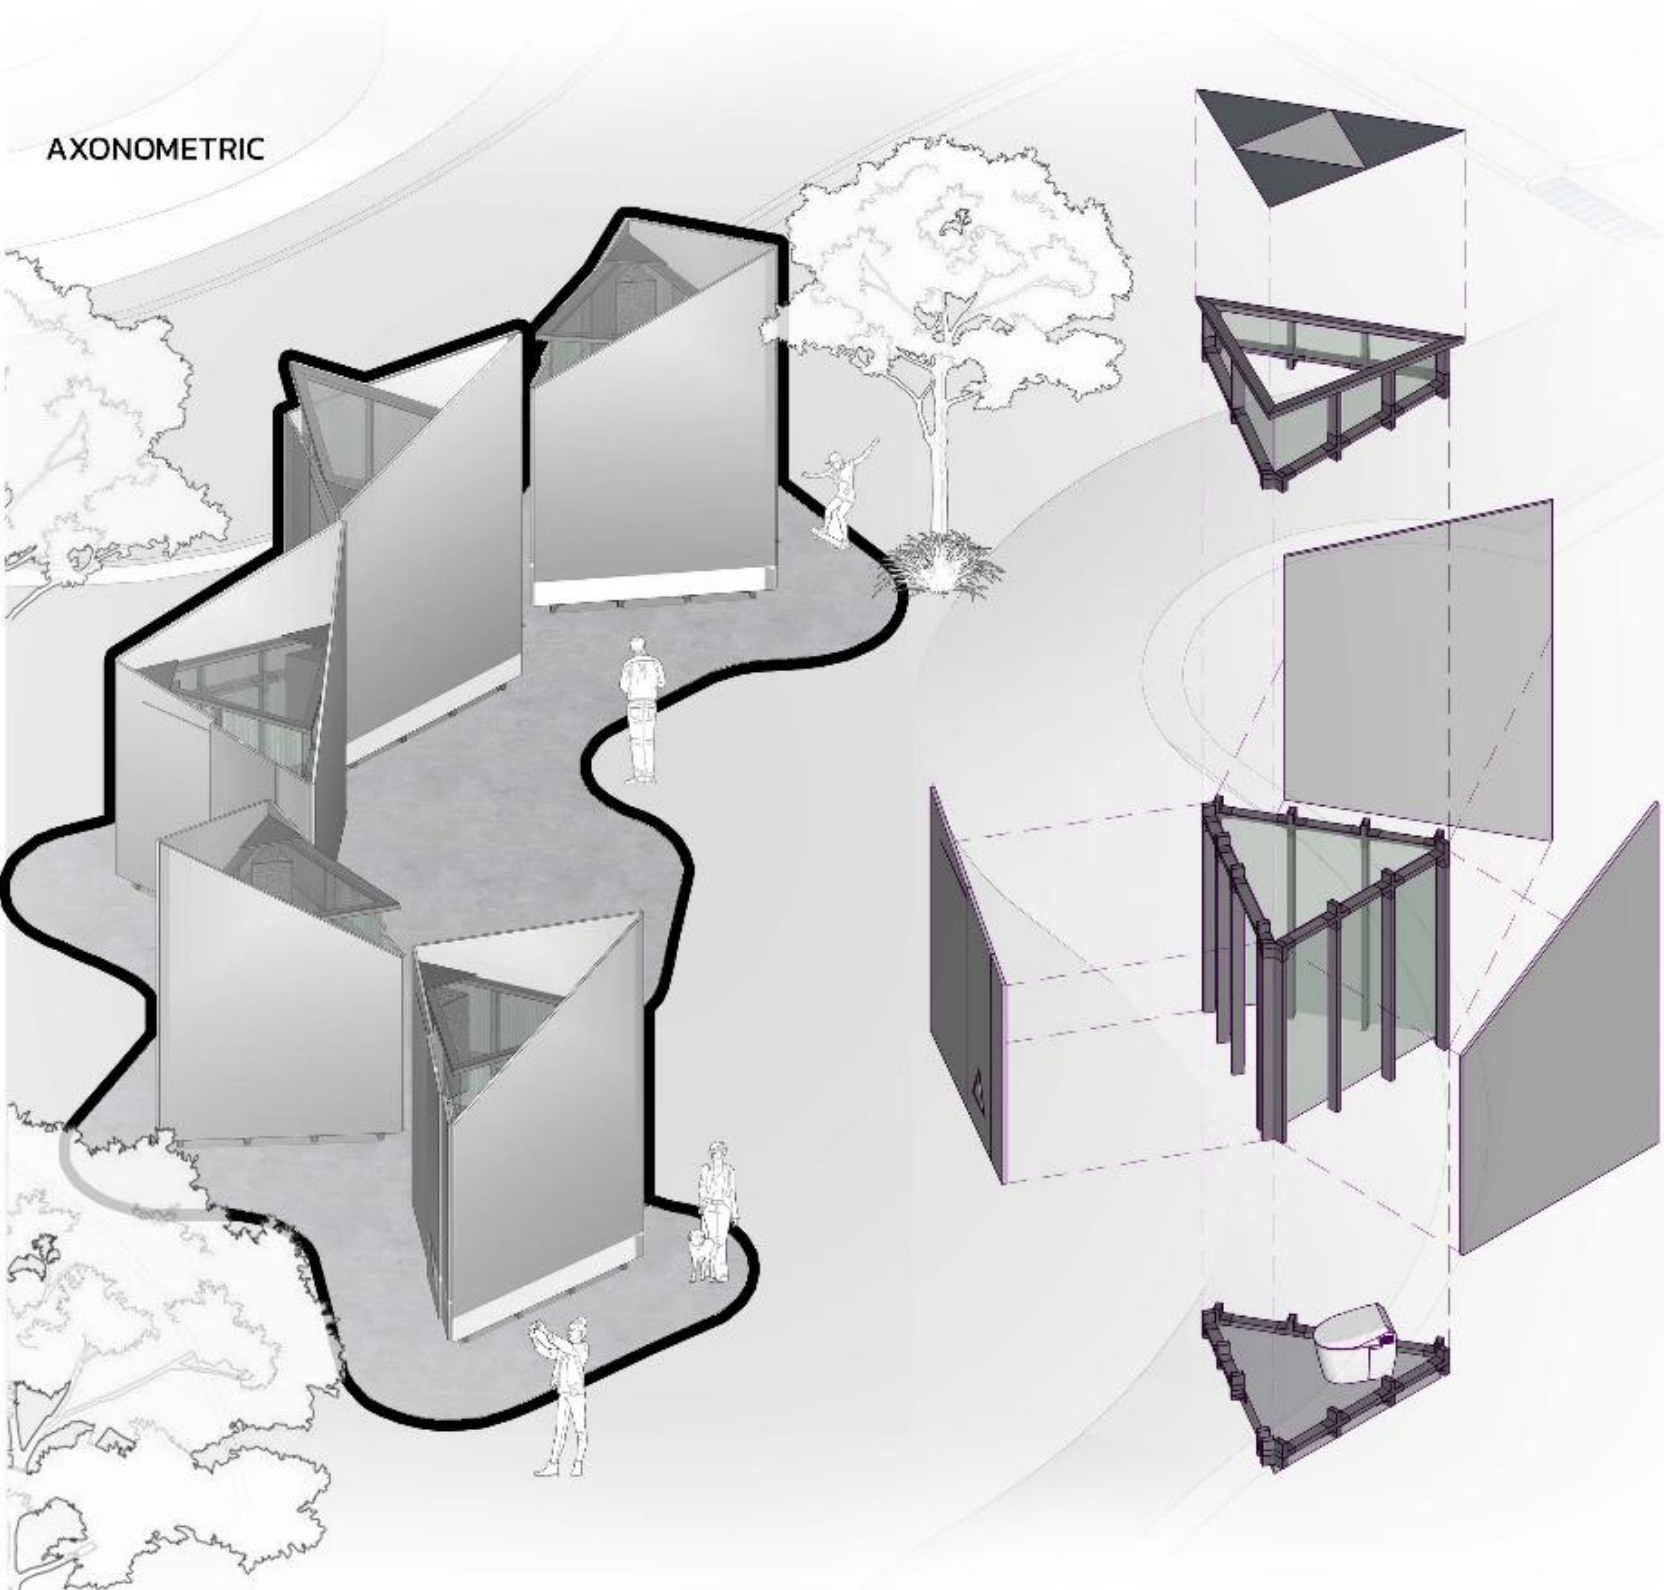


PERSPECTIVE

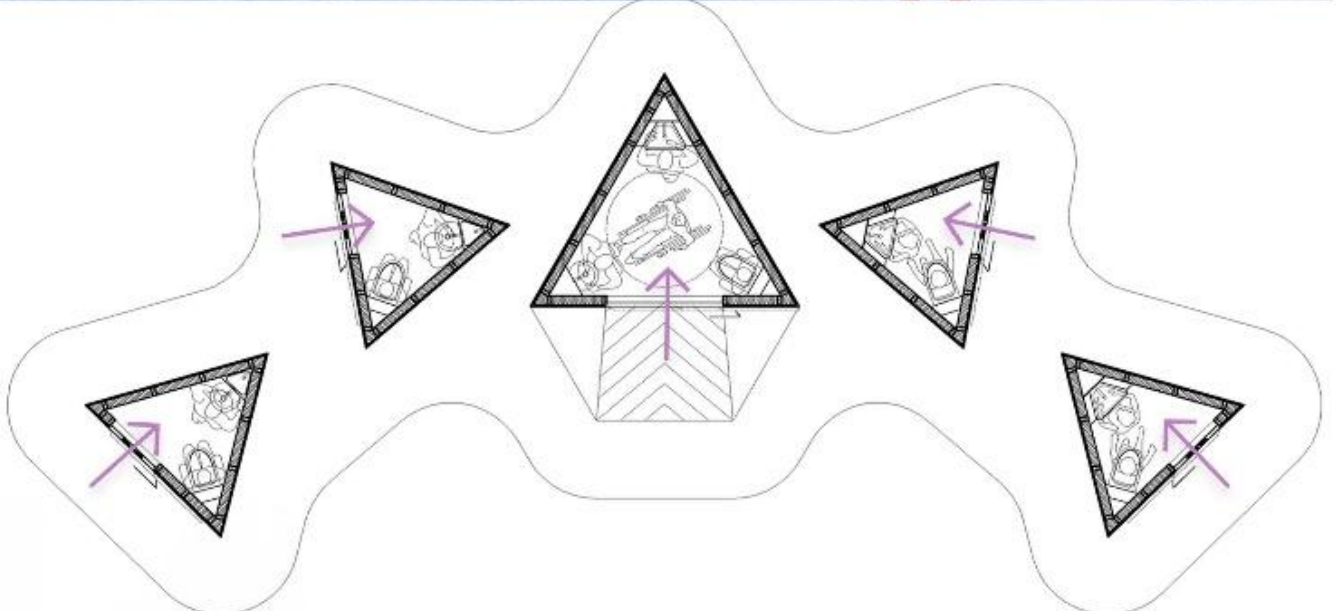


PLAN

เรียงตัวในลักษณะ: สบมาตรฐานมีห้องน้ำสาธารณะอยู่ตำแหน่งกลางแต่สัดส่วนของอาคารภายนอกไม่เท่ากัน ทำให้เกิด Art Visual ที่เข้ากับธรรมชาติ มีลักษณะเป็น Art Object อย่างหนึ่ง อีกทั้งใน Prototype ของ Green Area นี้ยังสามารถปรับเปลี่ยนรูปแบบให้สลับไหลไปกับพื้นที่จริงตาม Space ระหว่างต้นไม้ในรูปทรงต่างๆ ได้อีกด้วย

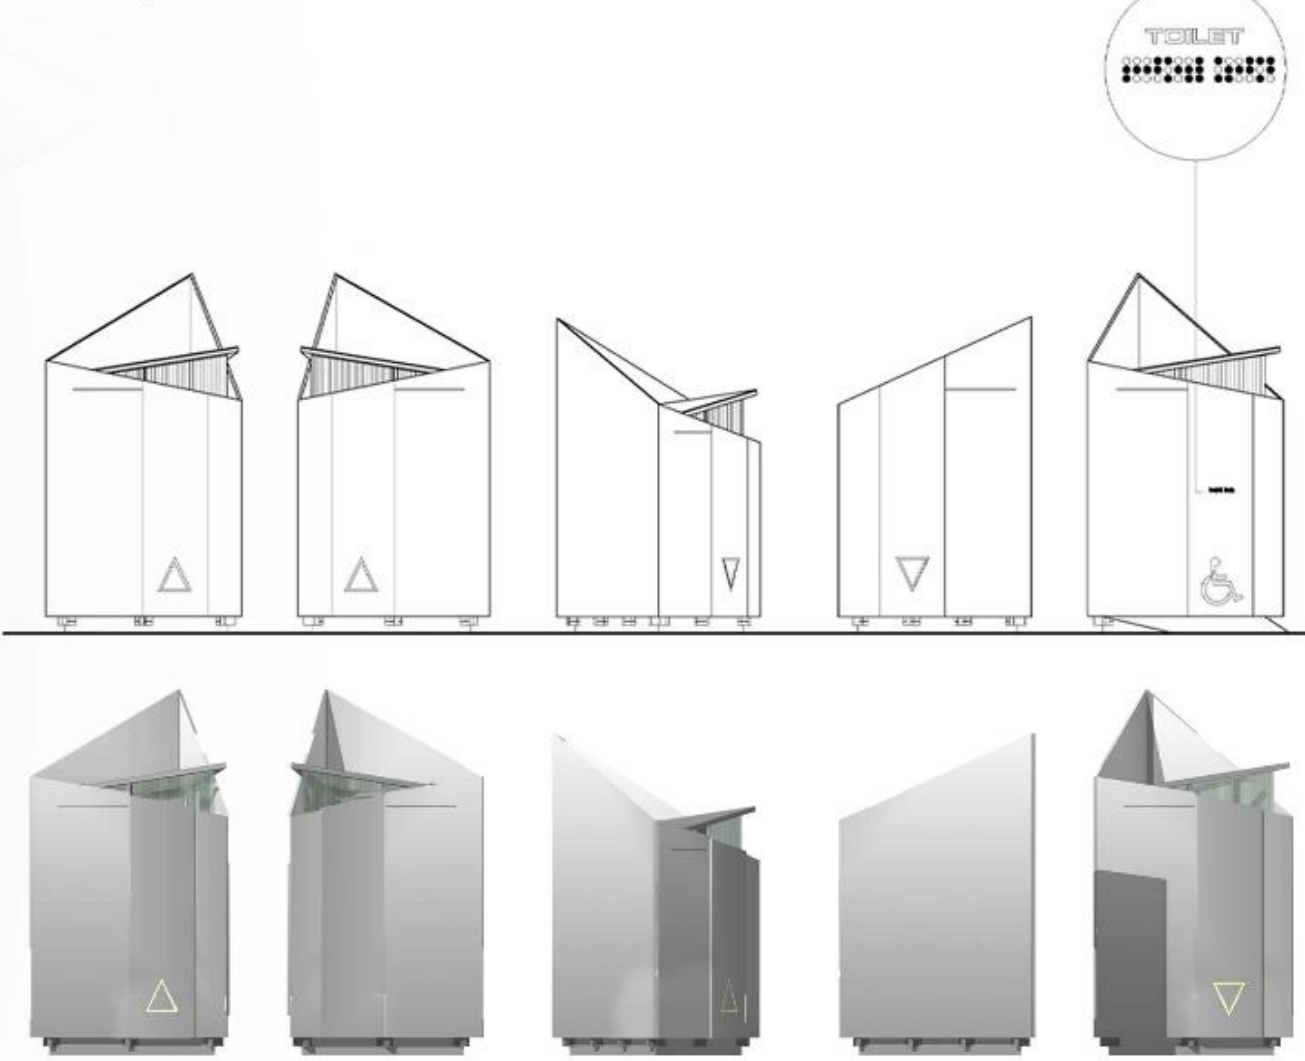

ELEVATION

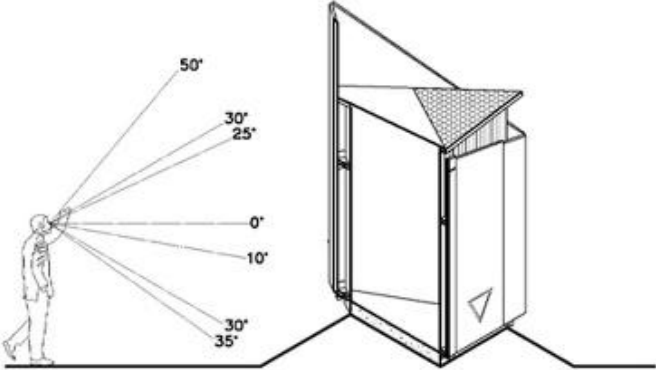

SECTION